

# Porous Habitat

Situato in un tranquillo villaggio di Sleman, Yogyakarta, a breve distanza da un'università privata locale, Porous Habitat è una edificio coliving di dodici unità che offre molto più di un semplice alloggio.

Il progetto risponde alla crescente domanda di spazi abitativi per studenti, integrandosi con naturalezza nello spirito del luogo.

L'architettura trae ispirazione dalla forma familiare del limasan, la tradizionale struttura a tetto inclinato diffusa nel quartiere.

Questo riferimento vernacolare viene reinterpretato in una volumetria essenziale che unisce brutalismo, ecoismo e regionalismo architettonico: un linguaggio che combina masse semplici e materiche, attenzione al clima tropicale e un profondo legame con le tradizioni costruttive locali.

I materiali scelti — grezzi, monolitici e privi di artifici — non cercano di emergere, ma di appartenere silenziosamente al paesaggio costruito, contribuendo a un'identità discreta e radicata nel territorio.

## APPARTAMENTI | COLIVING

Regionalismo | Brutalismo | Ecoismo



**Posizione:** Sleman, Yogyakarta - Indonesia

**Studio:** Inklusi.dsg



**Architetto principale:** Gilang Dwi Alridho

**Area:** 266 m<sup>2</sup>


**Anno:** 2023

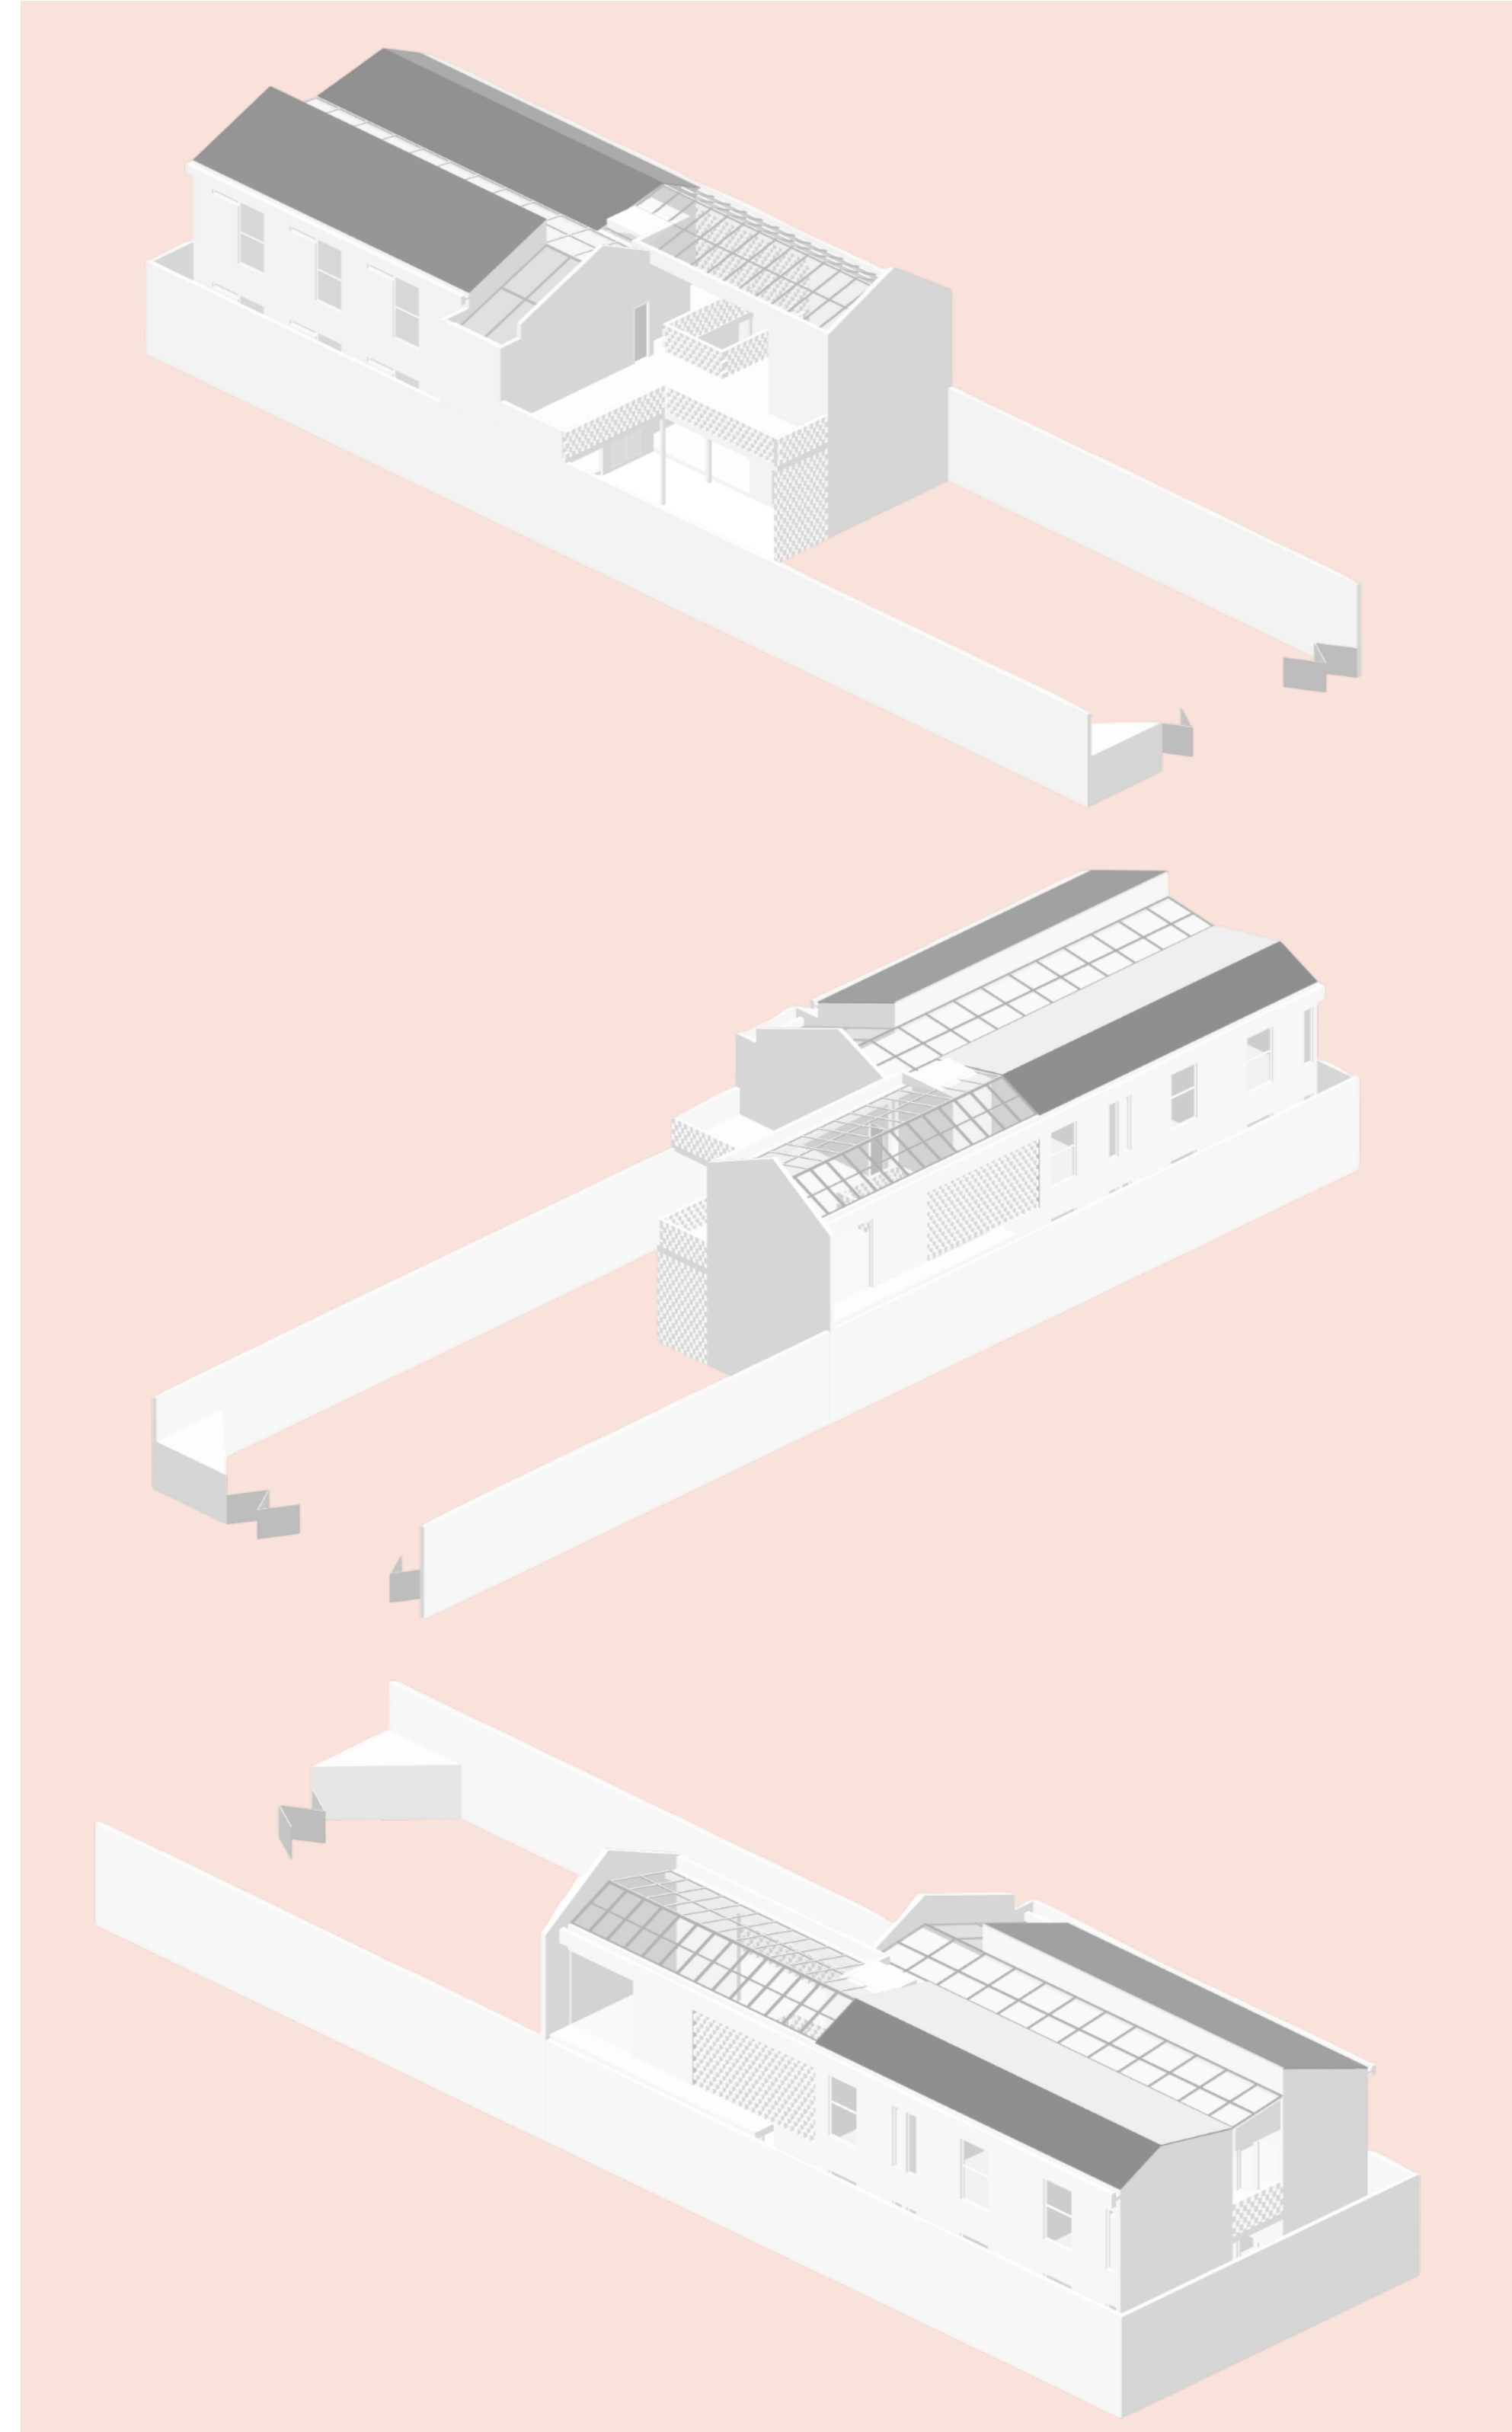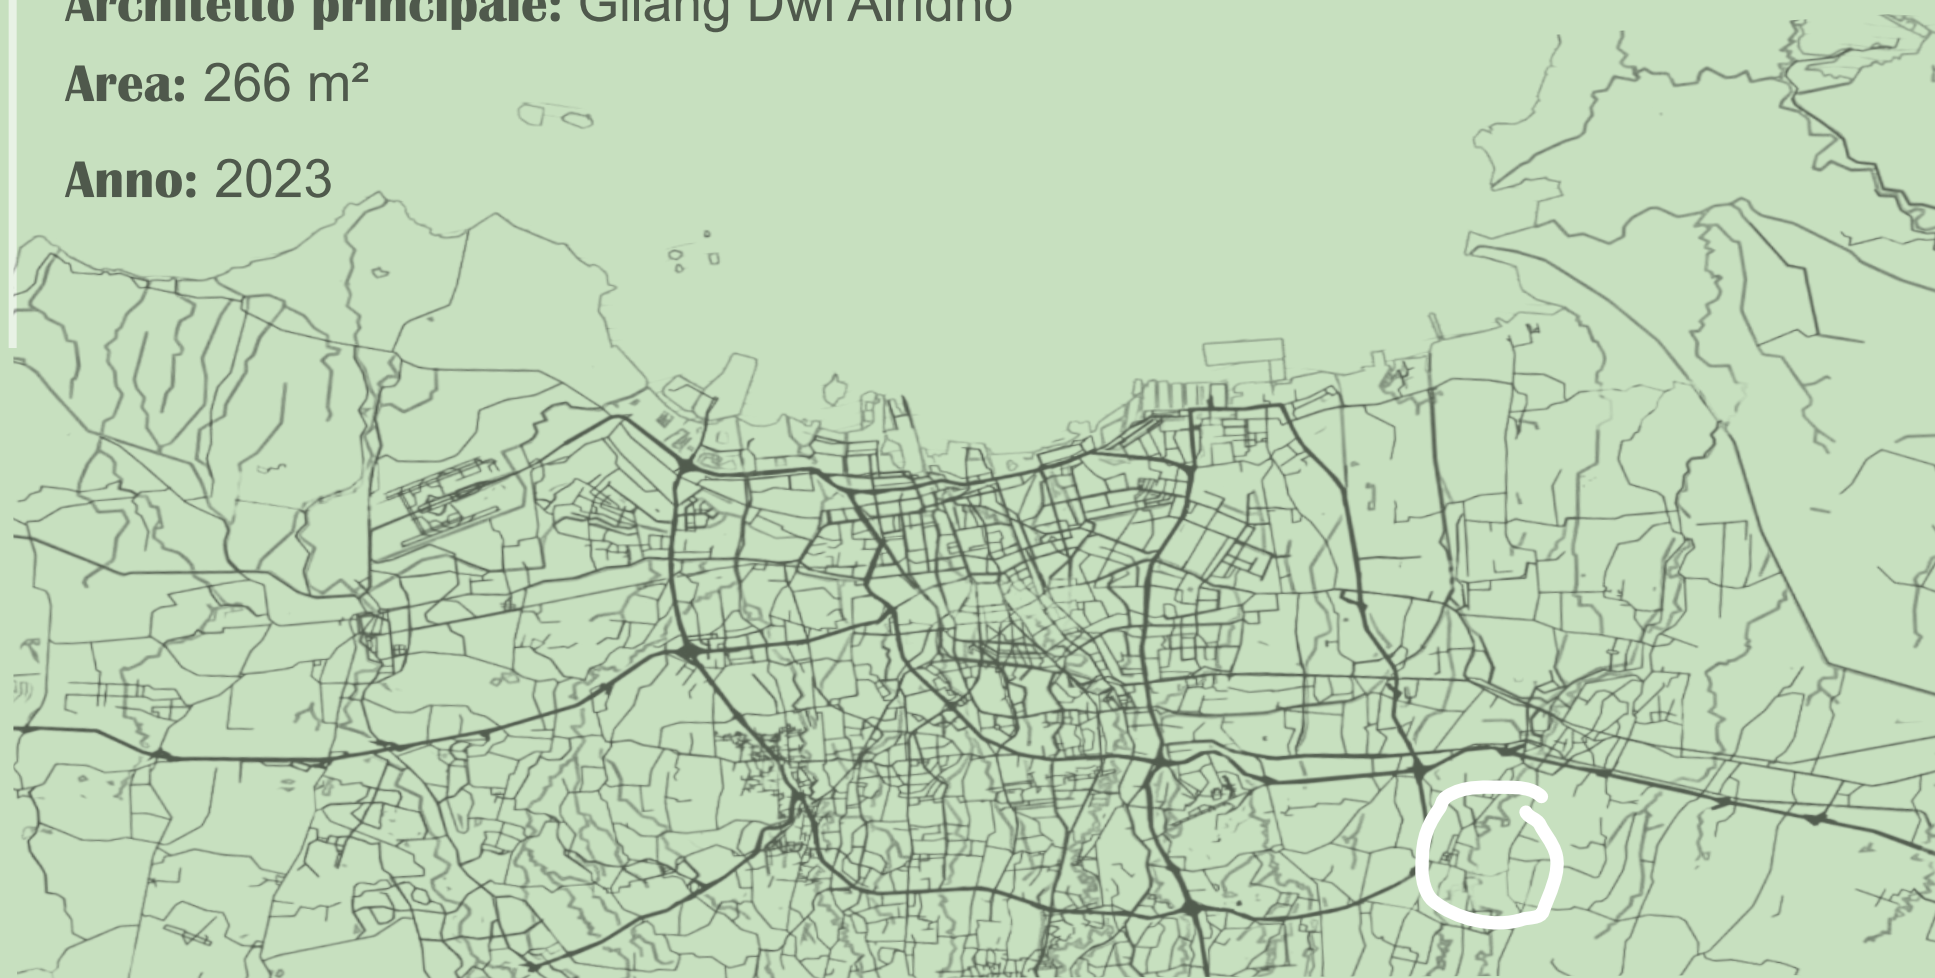

Prospetto D-D'

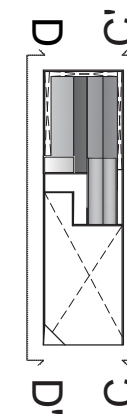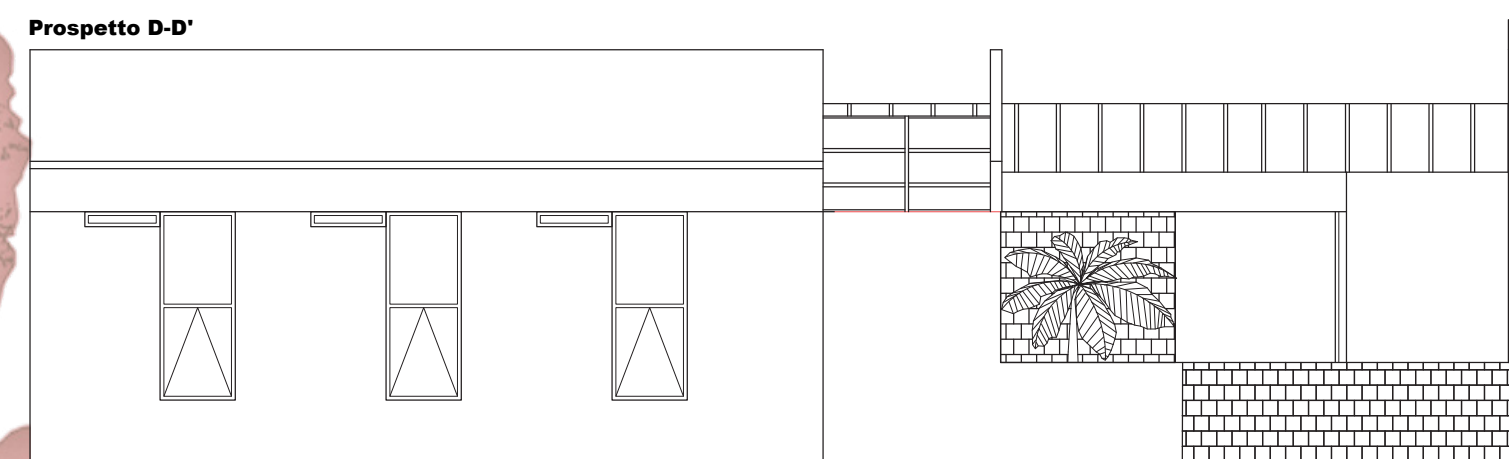

Prospetto C-C'

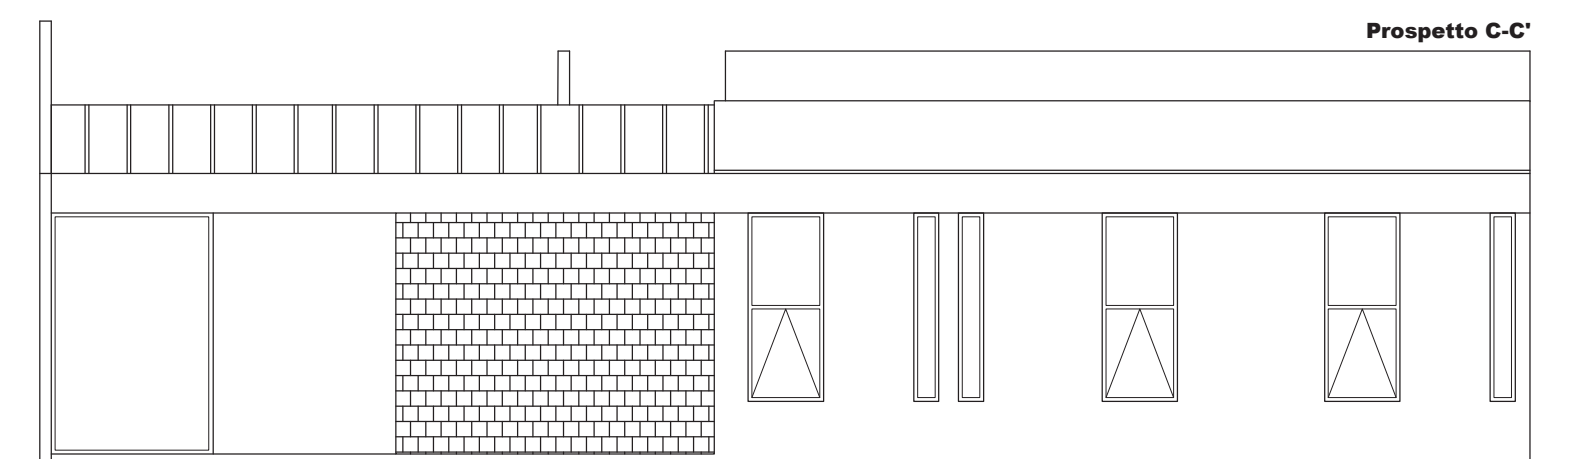



# Porous Habitat


La distribuzione interna combina spazi privati e aree condivise: sei camere sono dotate di bagno esclusivo, mentre le restanti usufruiscono di servizi igienici comuni, organizzati per garantire comfort e funzionalità.

All'interno, le stanze — con superfici variabili tra 9 e 12 m<sup>2</sup> — sono dotate di due aperture contrapposte che favoriscono la ventilazione trasversale. Questa soluzione permette l'ingresso di aria fresca, luce naturale e viste verso l'esterno, mantenendo al contempo un elevato livello di privacy.

Gli spazi comuni includono una cucina condivisa completamente attrezzata, un'area dedicata all'attività fisica e uno spazio studio pensato per il lavoro individuale e collettivo.

All'esterno, il complesso dispone di un parcheggio riservato a moto e automobili, facilitando l'accesso e la mobilità degli utenti.

L'insieme degli ambienti mira a creare un equilibrio tra vita privata e comunitaria, integrando le esigenze abitative studentili con la tradizione indonesiana.

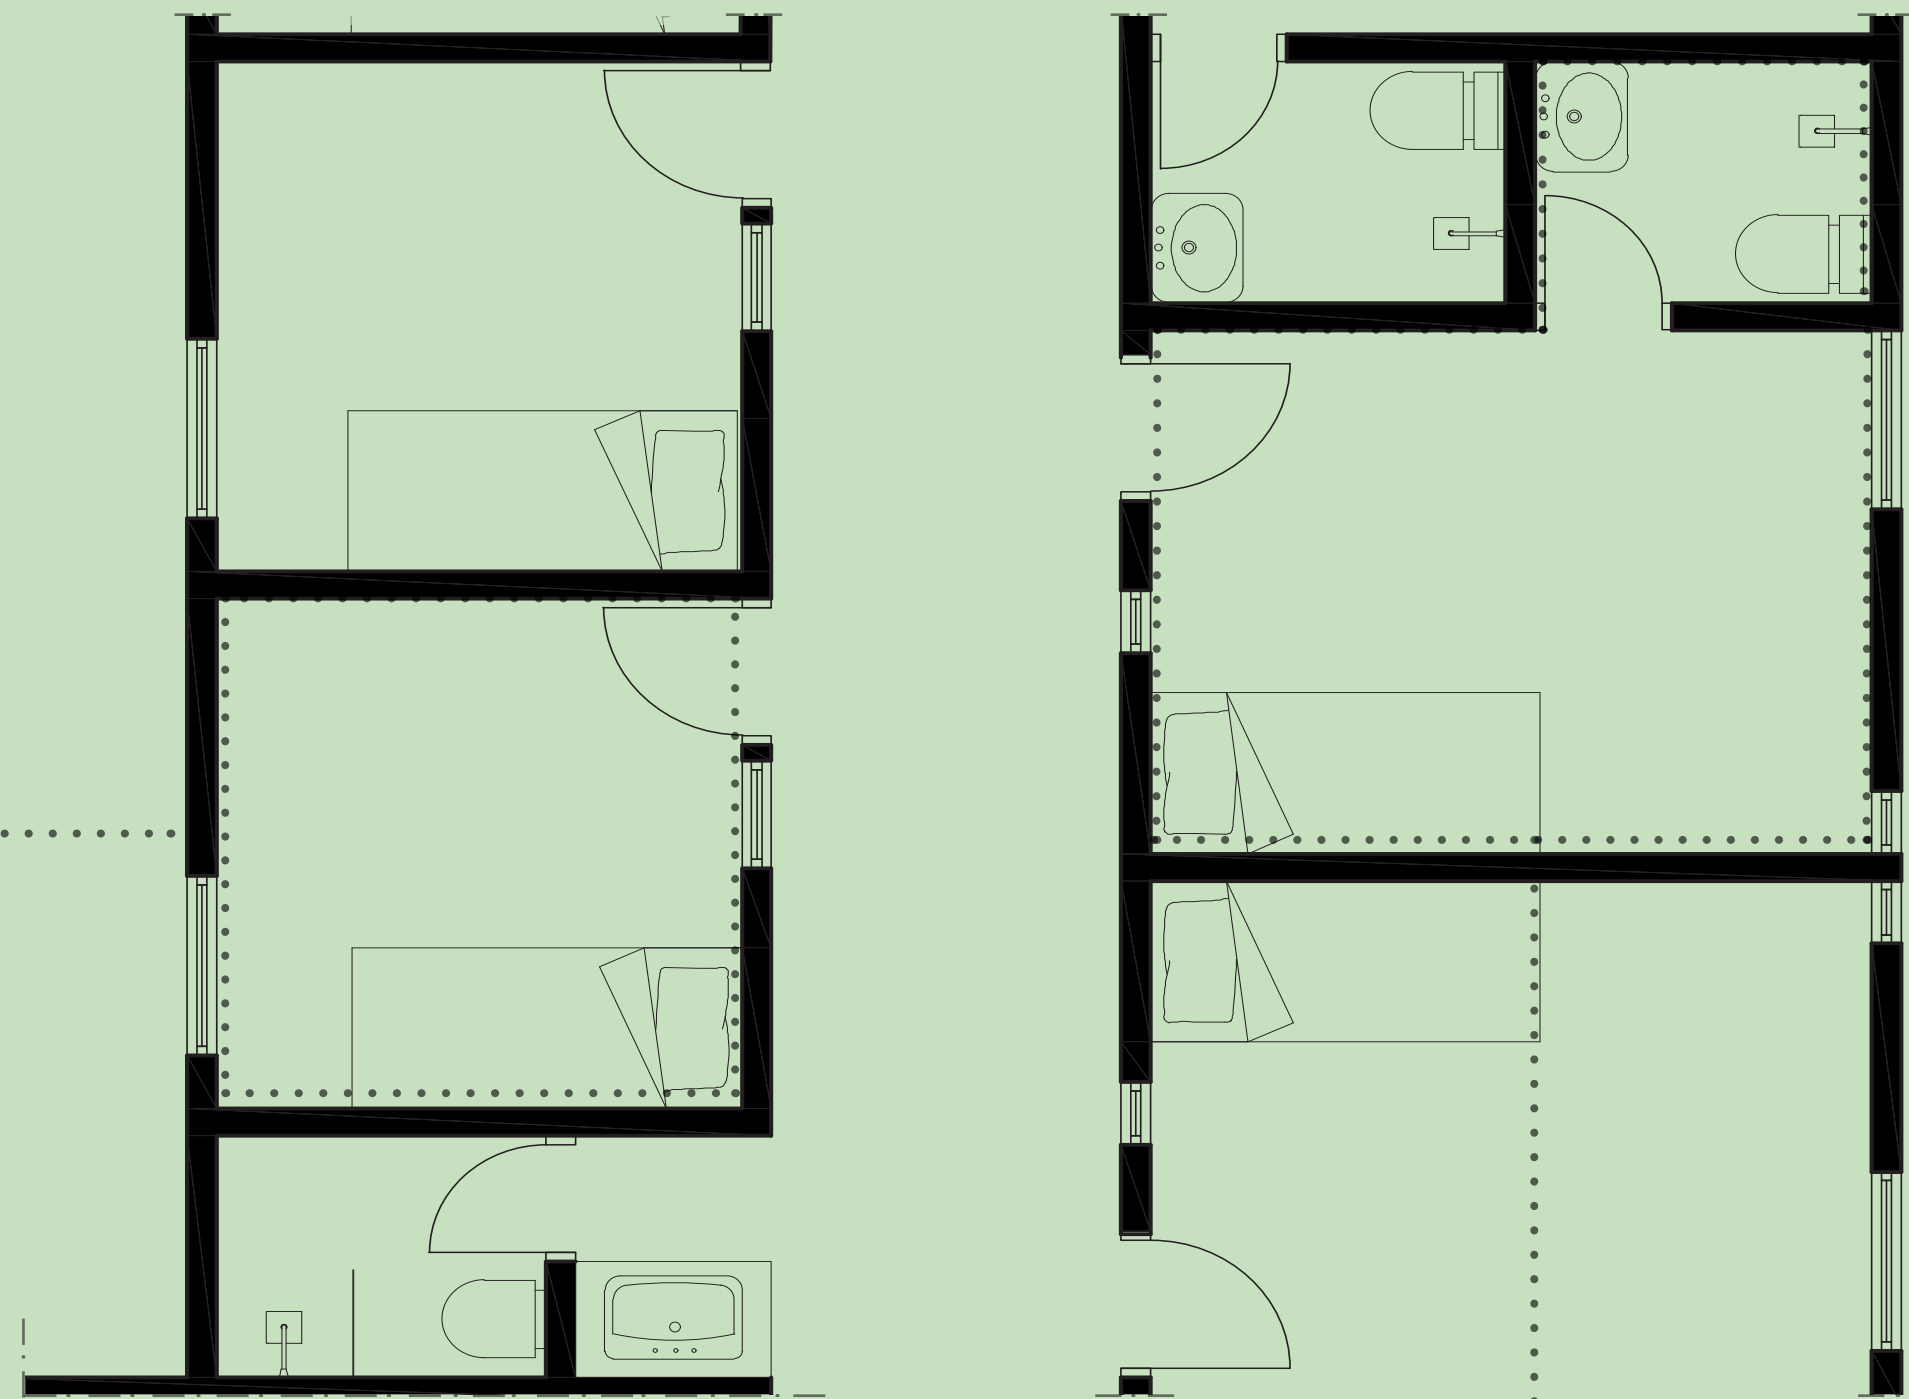

Scala 1:100

